



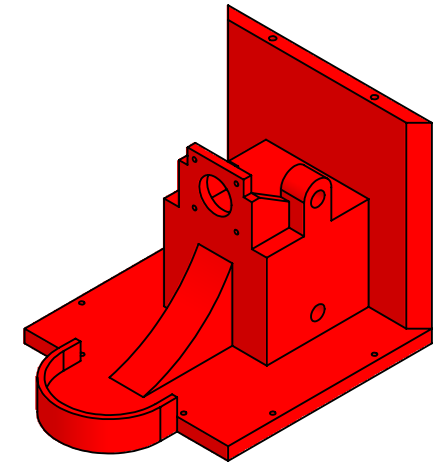

ISOMETRIC VIEW
SCALE: 1:4

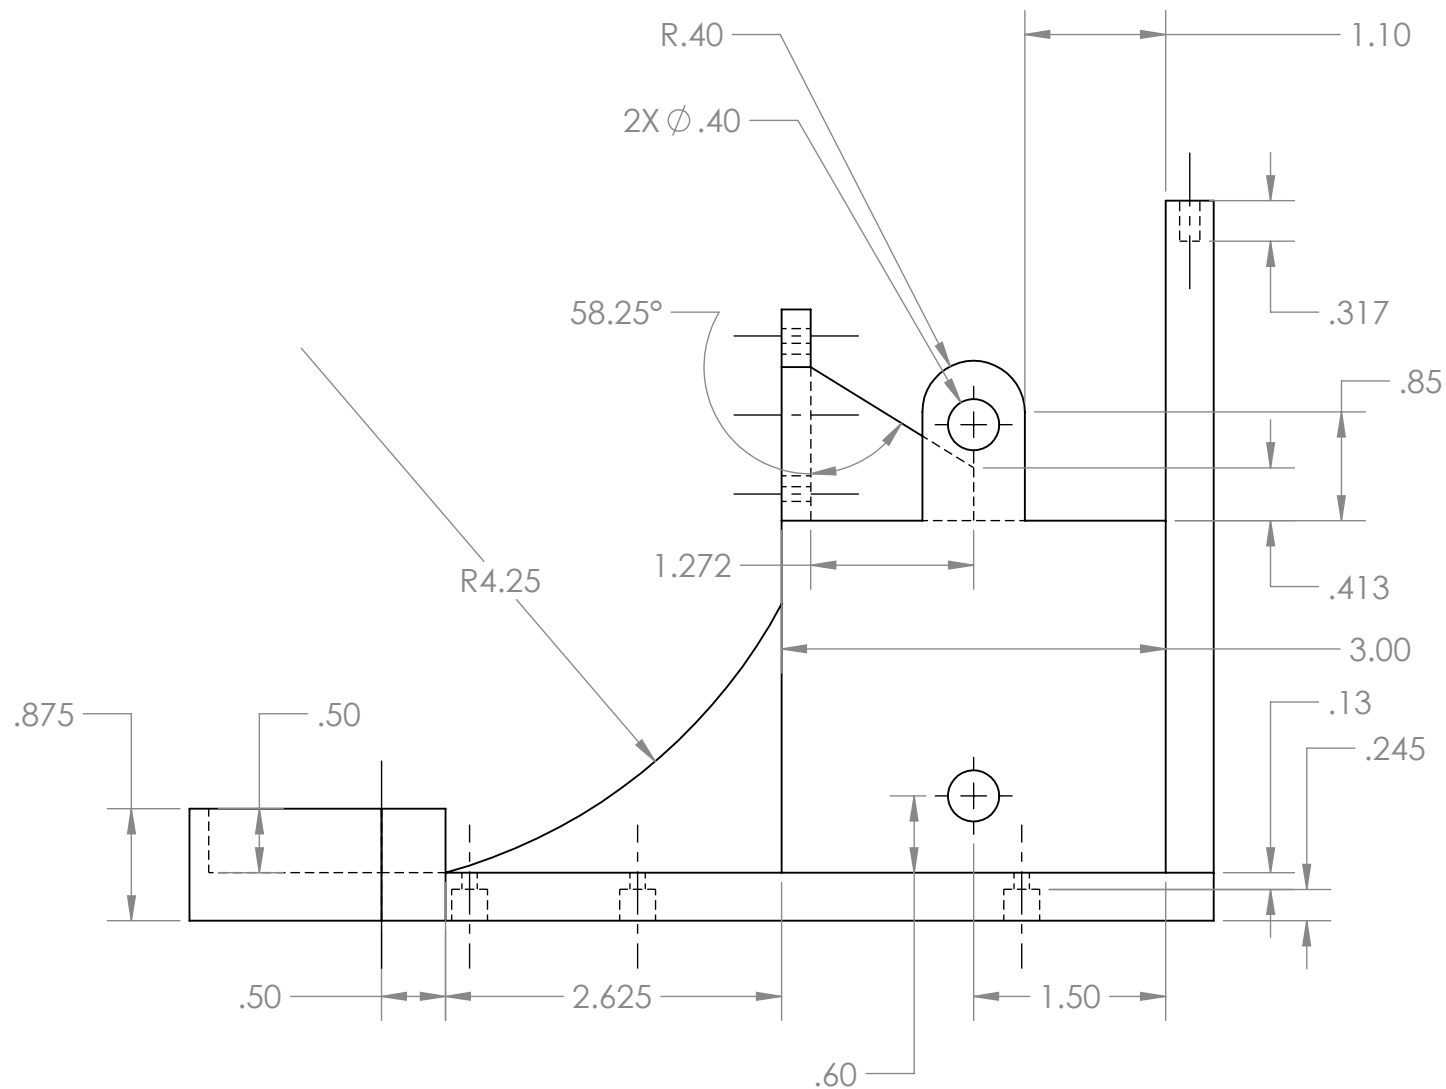

TITLE: Base Structure - Side View

DRAWN BY: Caleb Chapman

NOTES:
ALL DIMENSIONS IN INCHES
DO NOT SCALE DRAWING
PRINT WITH SUPPORTS

PROJECT: The Sugar Vault

FILE: SV_base

SHEET 02 OF 03

SCALE: 1:1.5

UNITS: IPS

REV: A

DWG #: SV-BASE-02

DATE: 7/21/2026

