



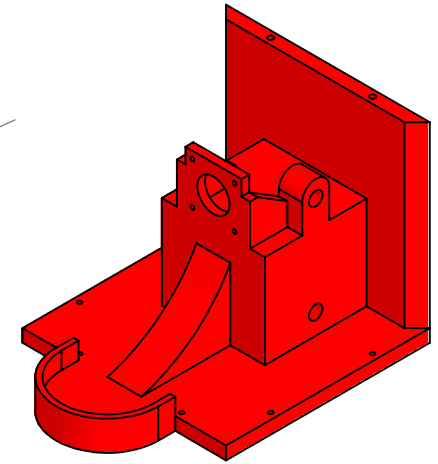

ISOMETRIC VIEW
SCALE: 1:4

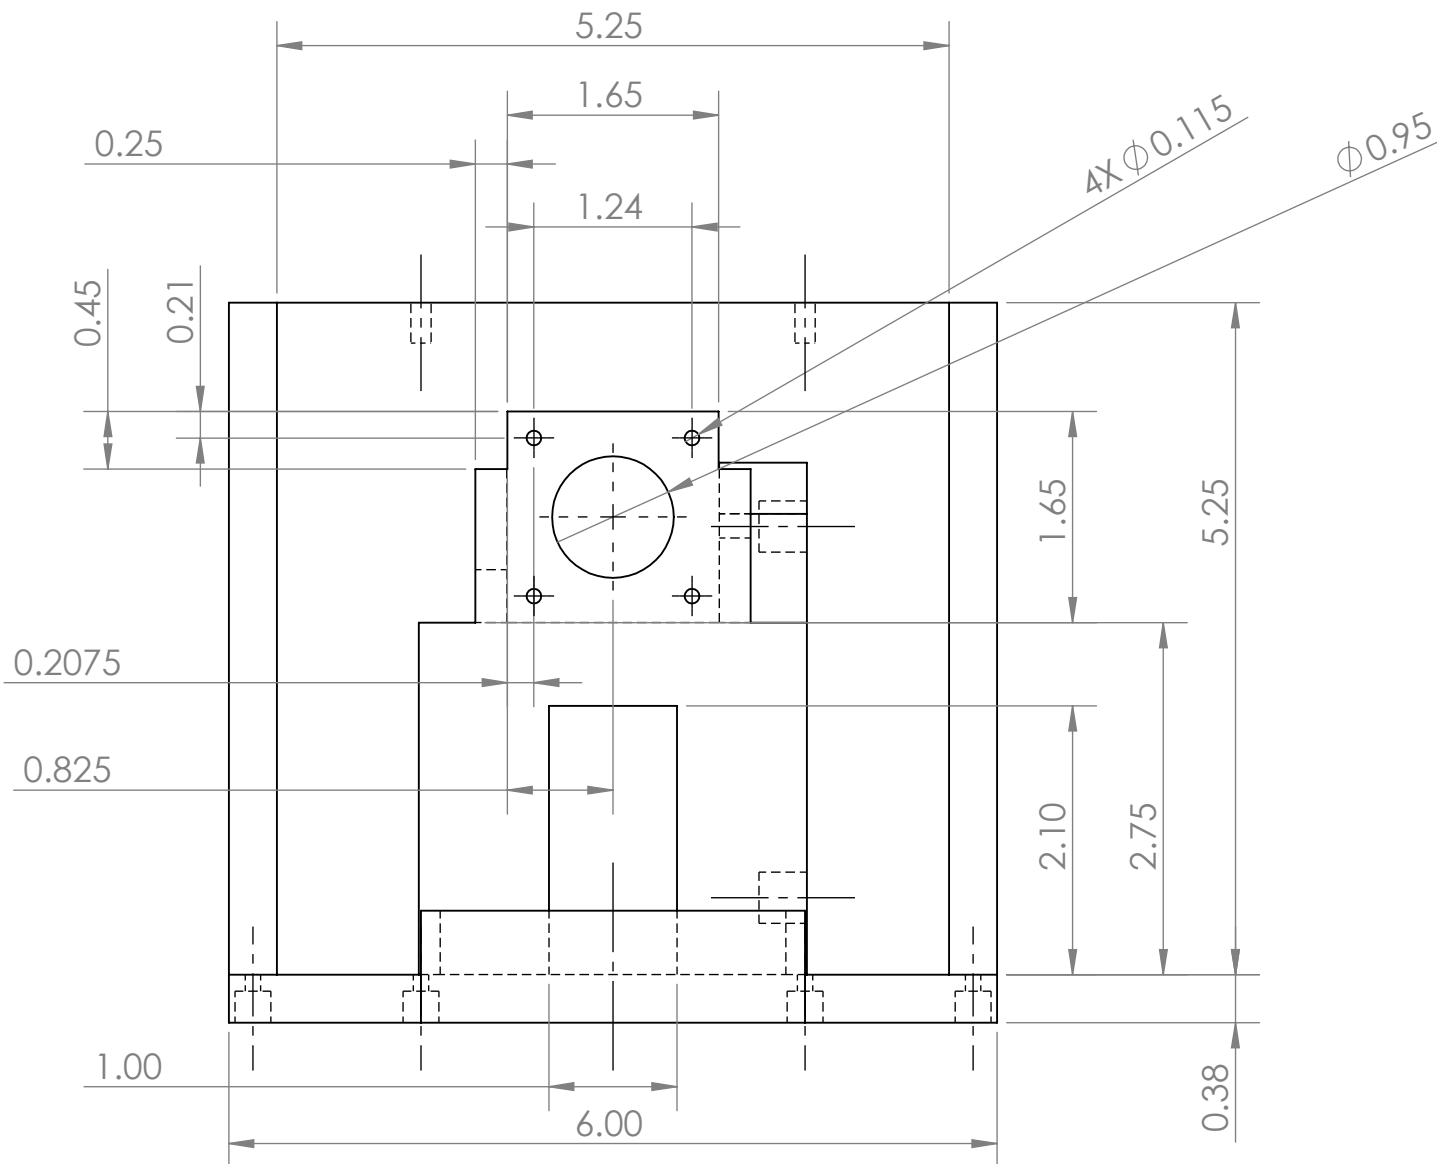

TITLE: Base Structure - Front View

DRAWN BY: Caleb Chapman

NOTES:

ALL DIMENSIONS IN INCHES
DO NOT SCALE DRAWING
PRINT WITH SUPPORTS

PROJECT: The Sugar Vault

FILE: SV_base

SHEET 01 **OF** 03

SCALE: 1:1.5

UNITS: IPS

REV: A

DWG #: SV-BASE-01

DATE: 7/21/2026

